






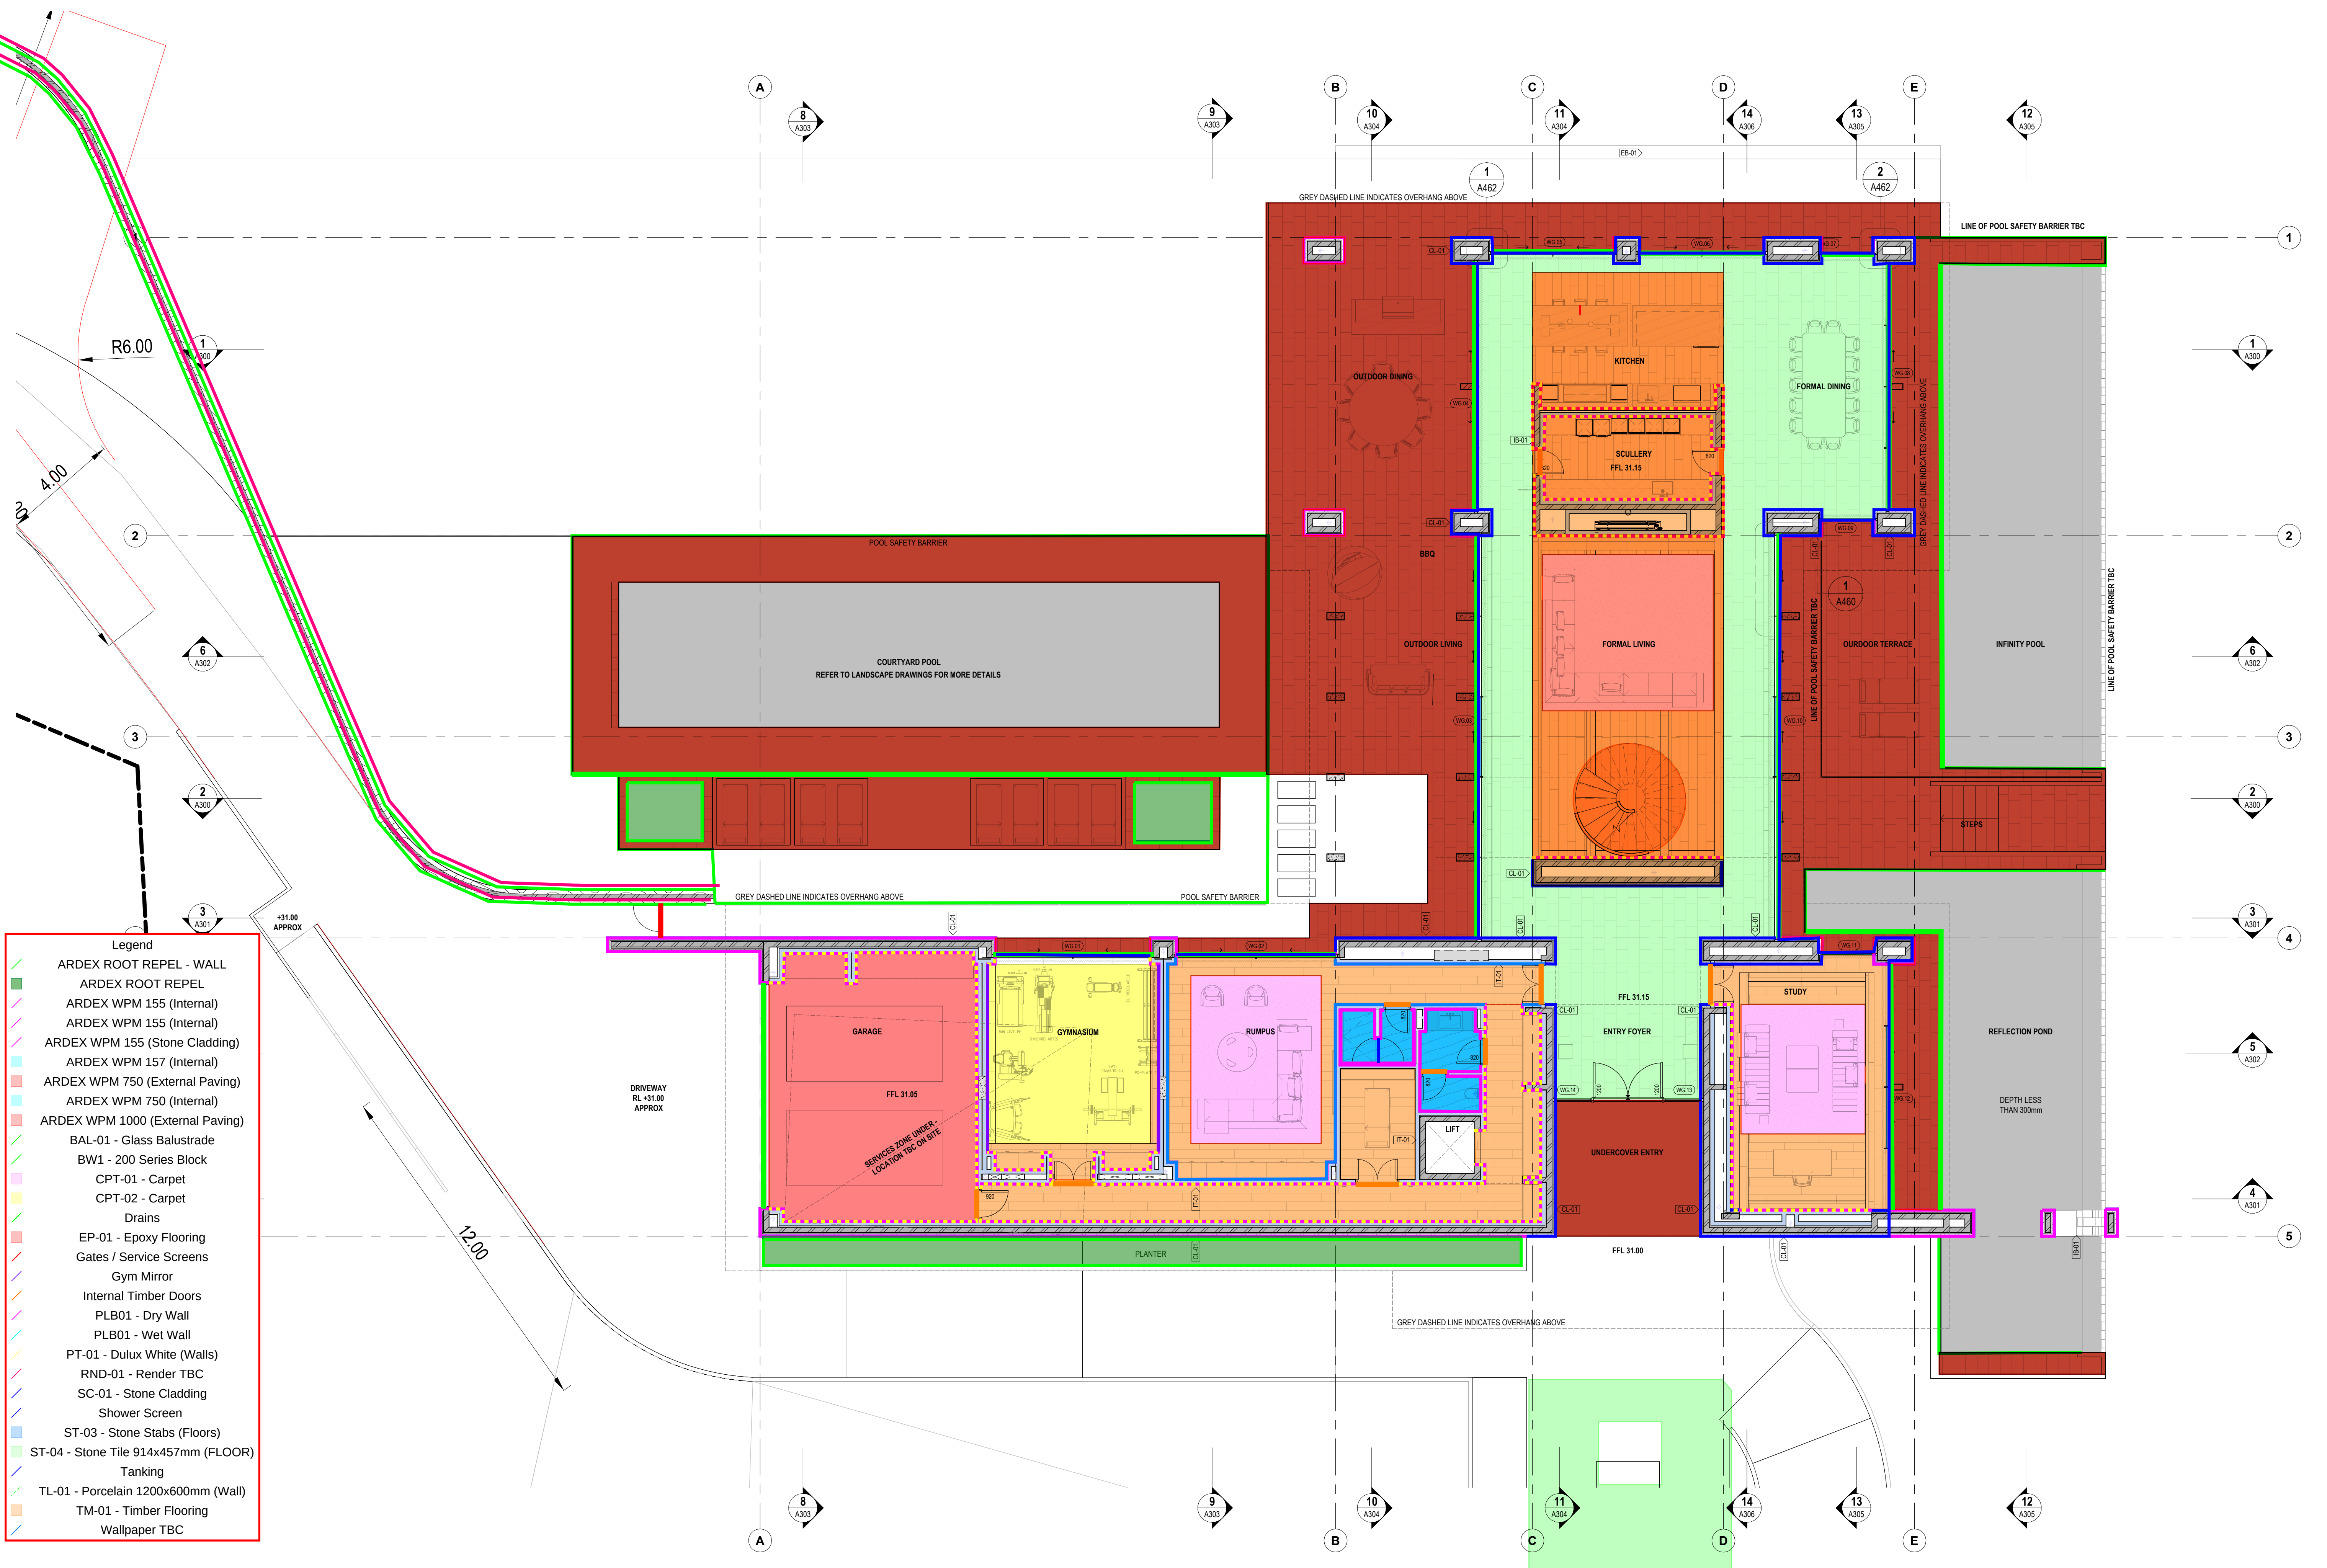

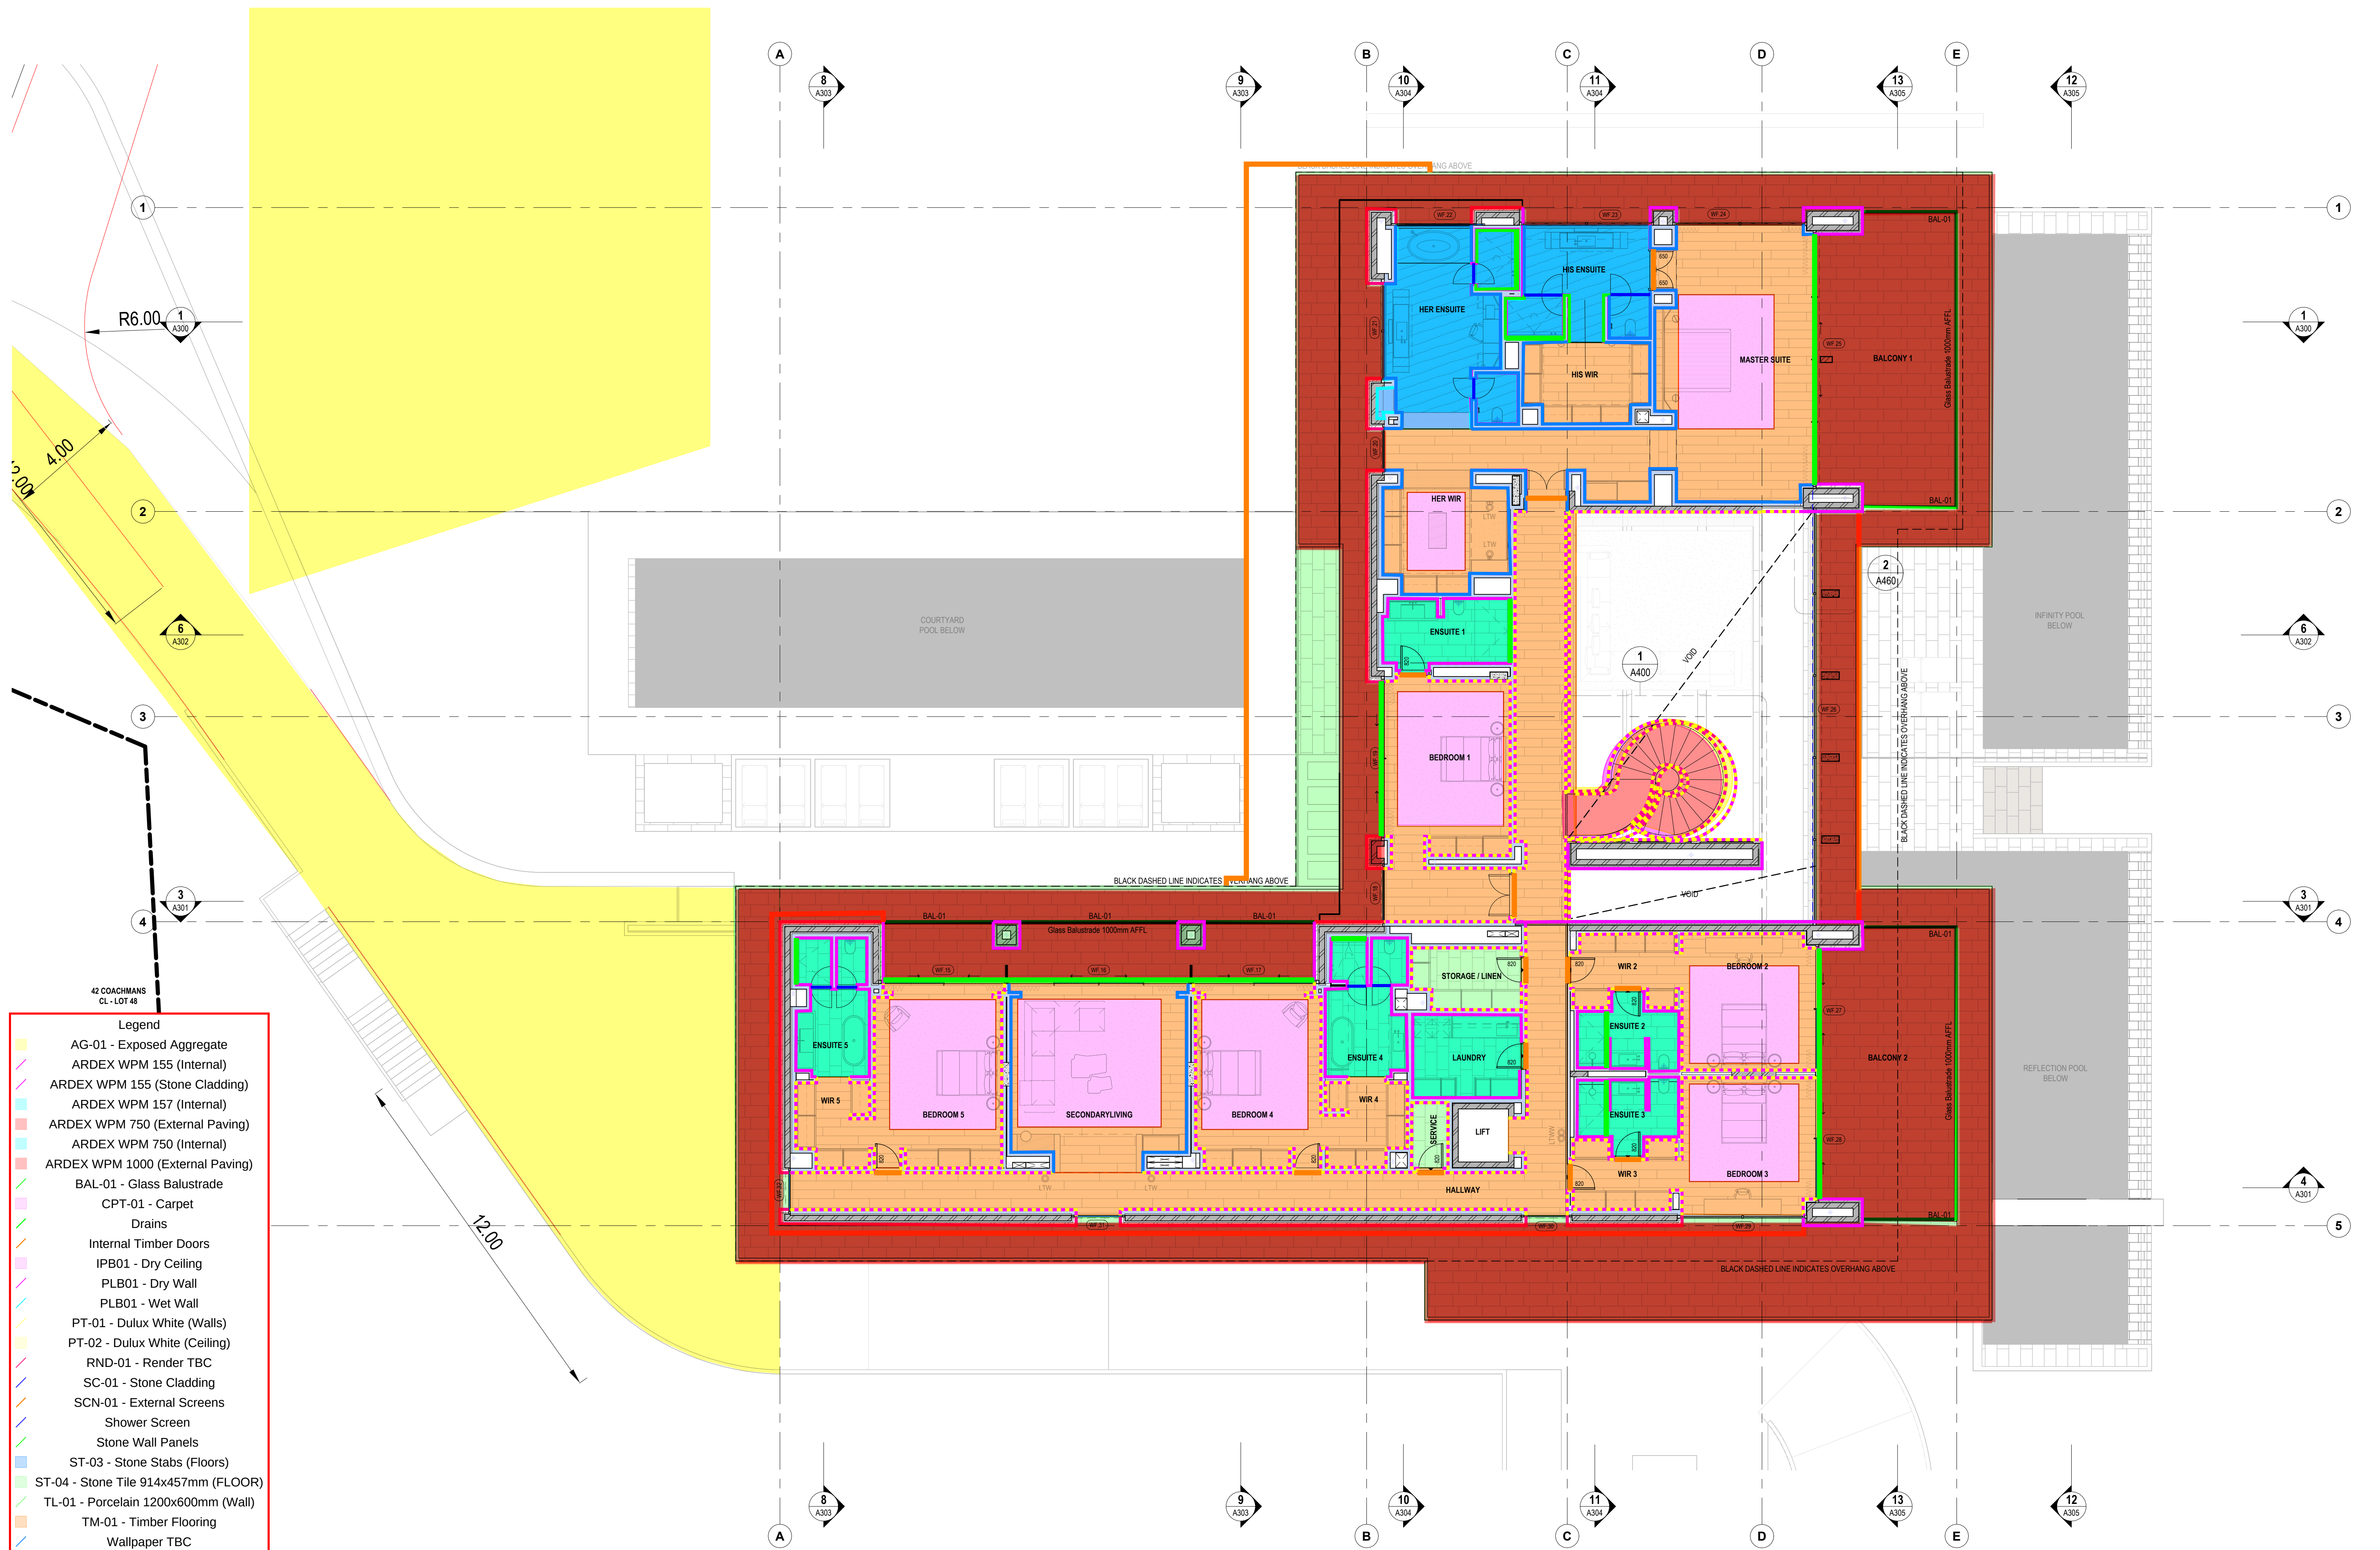

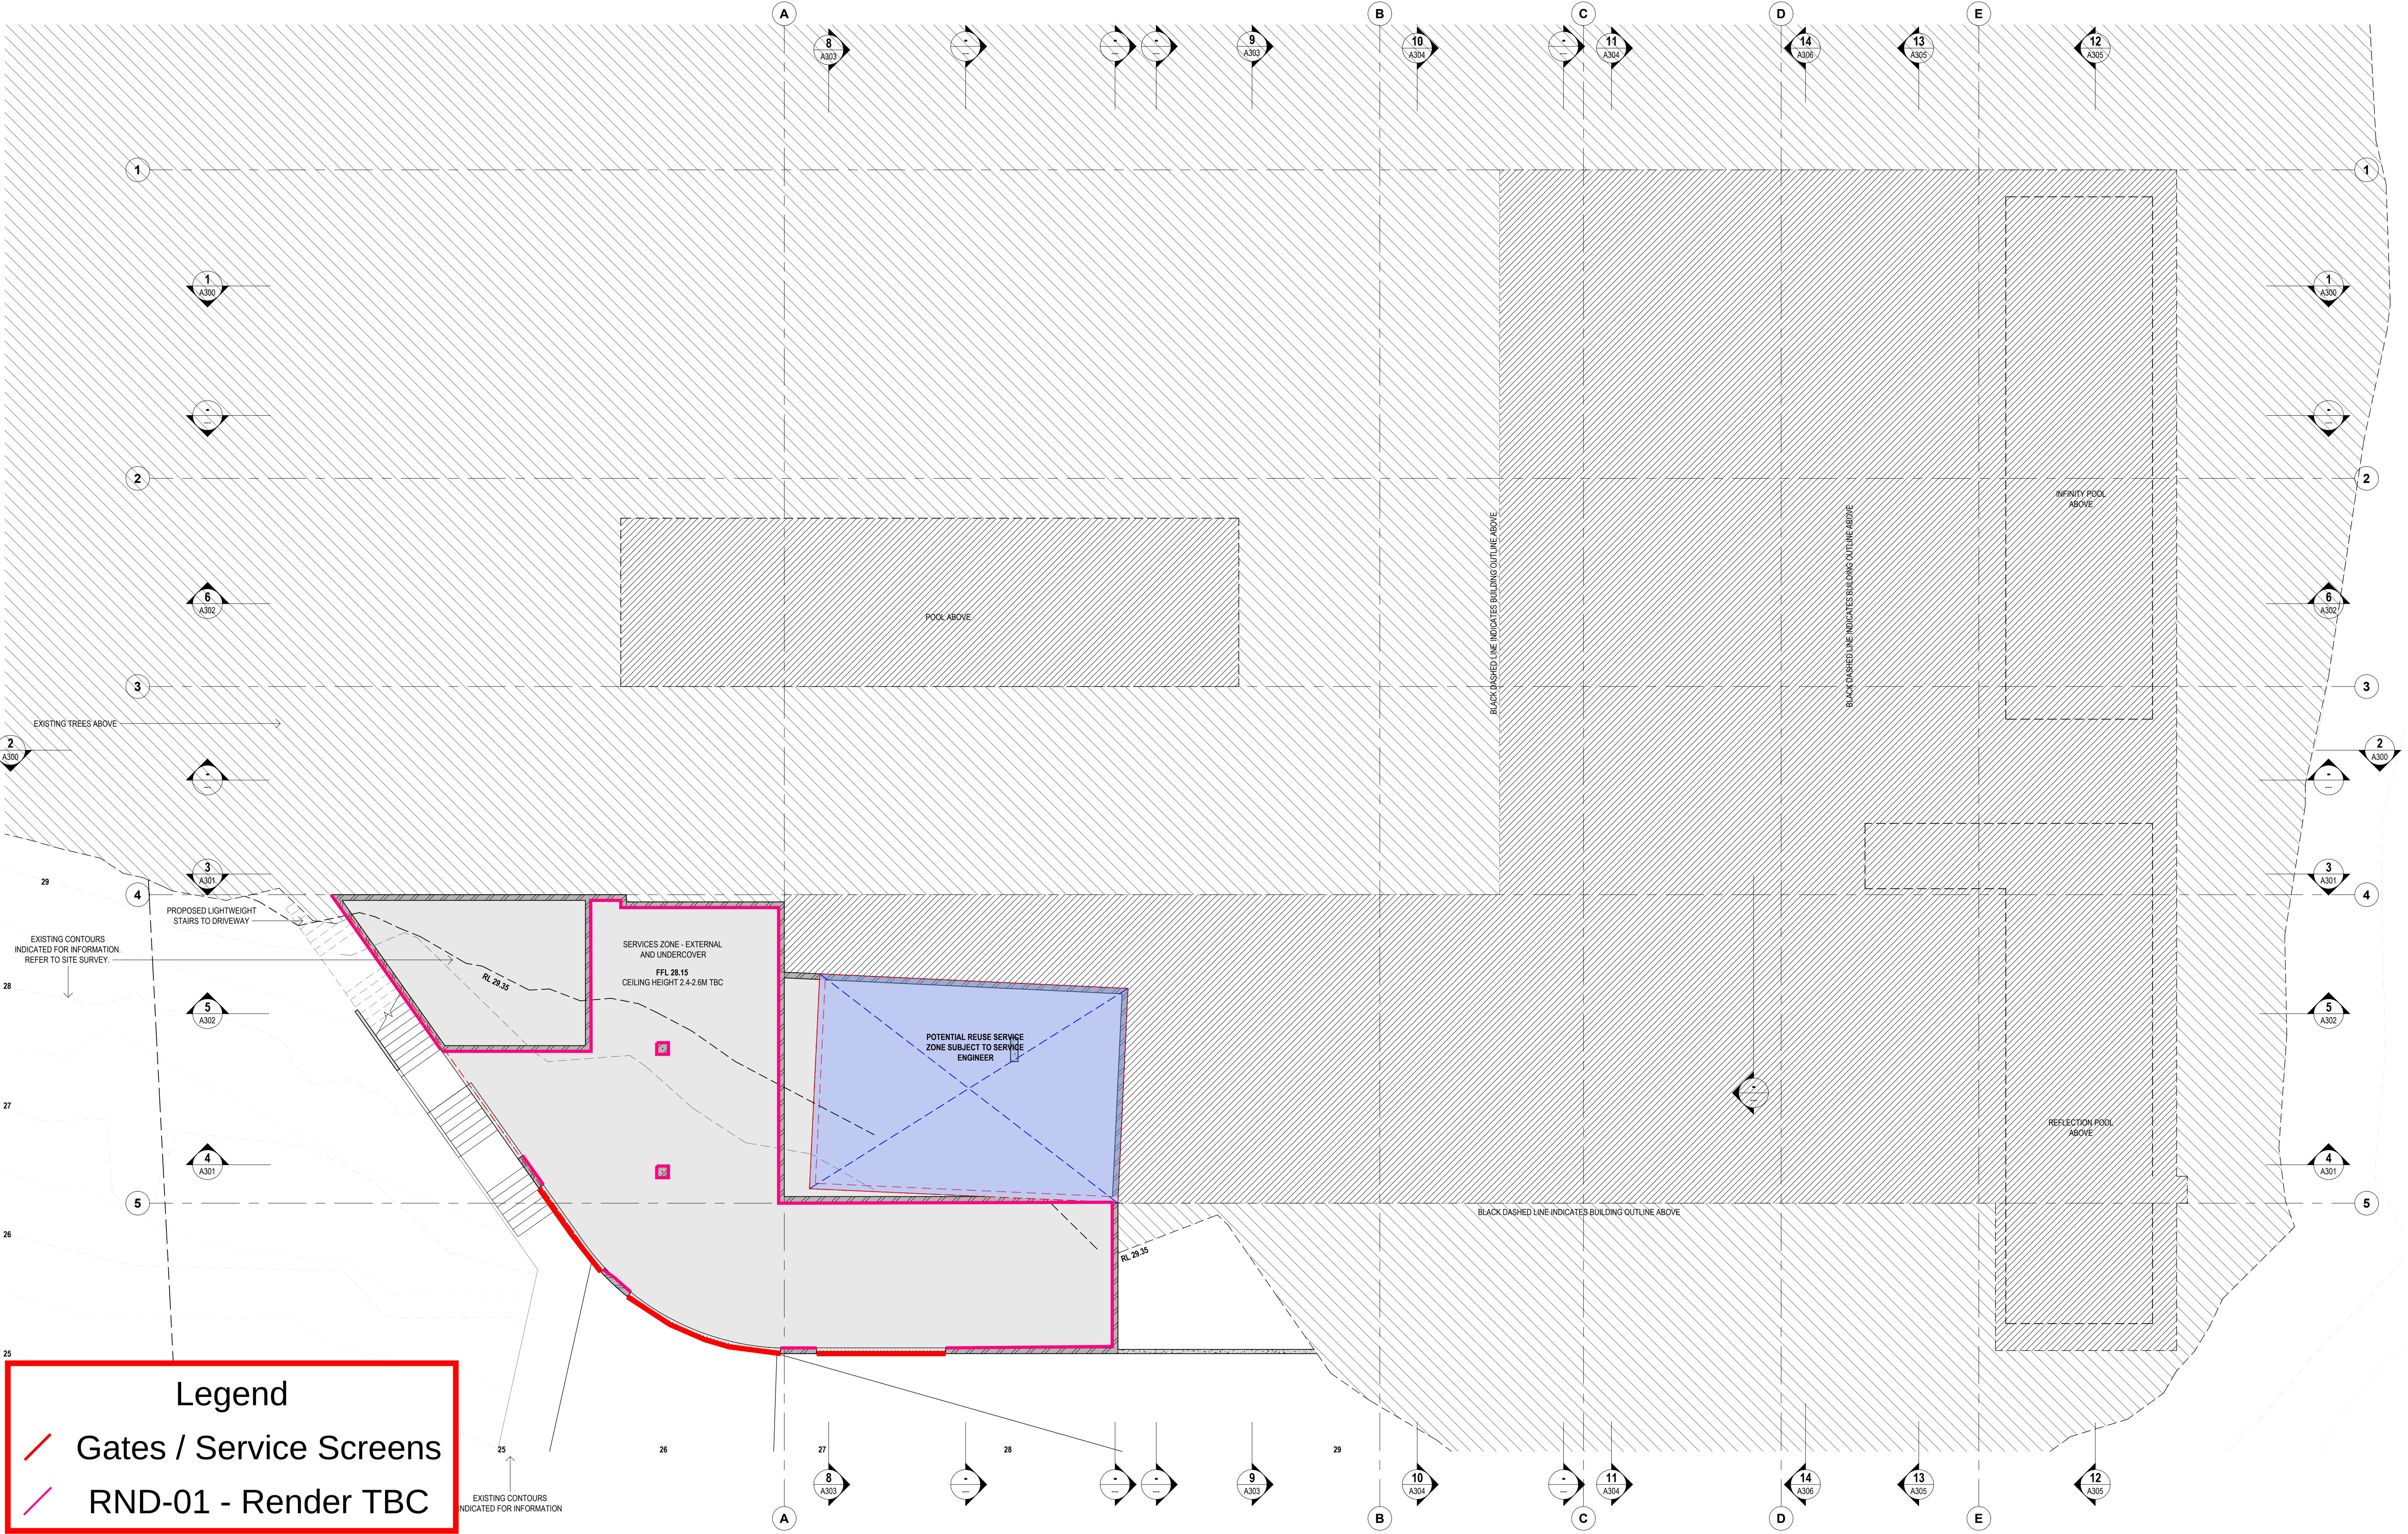

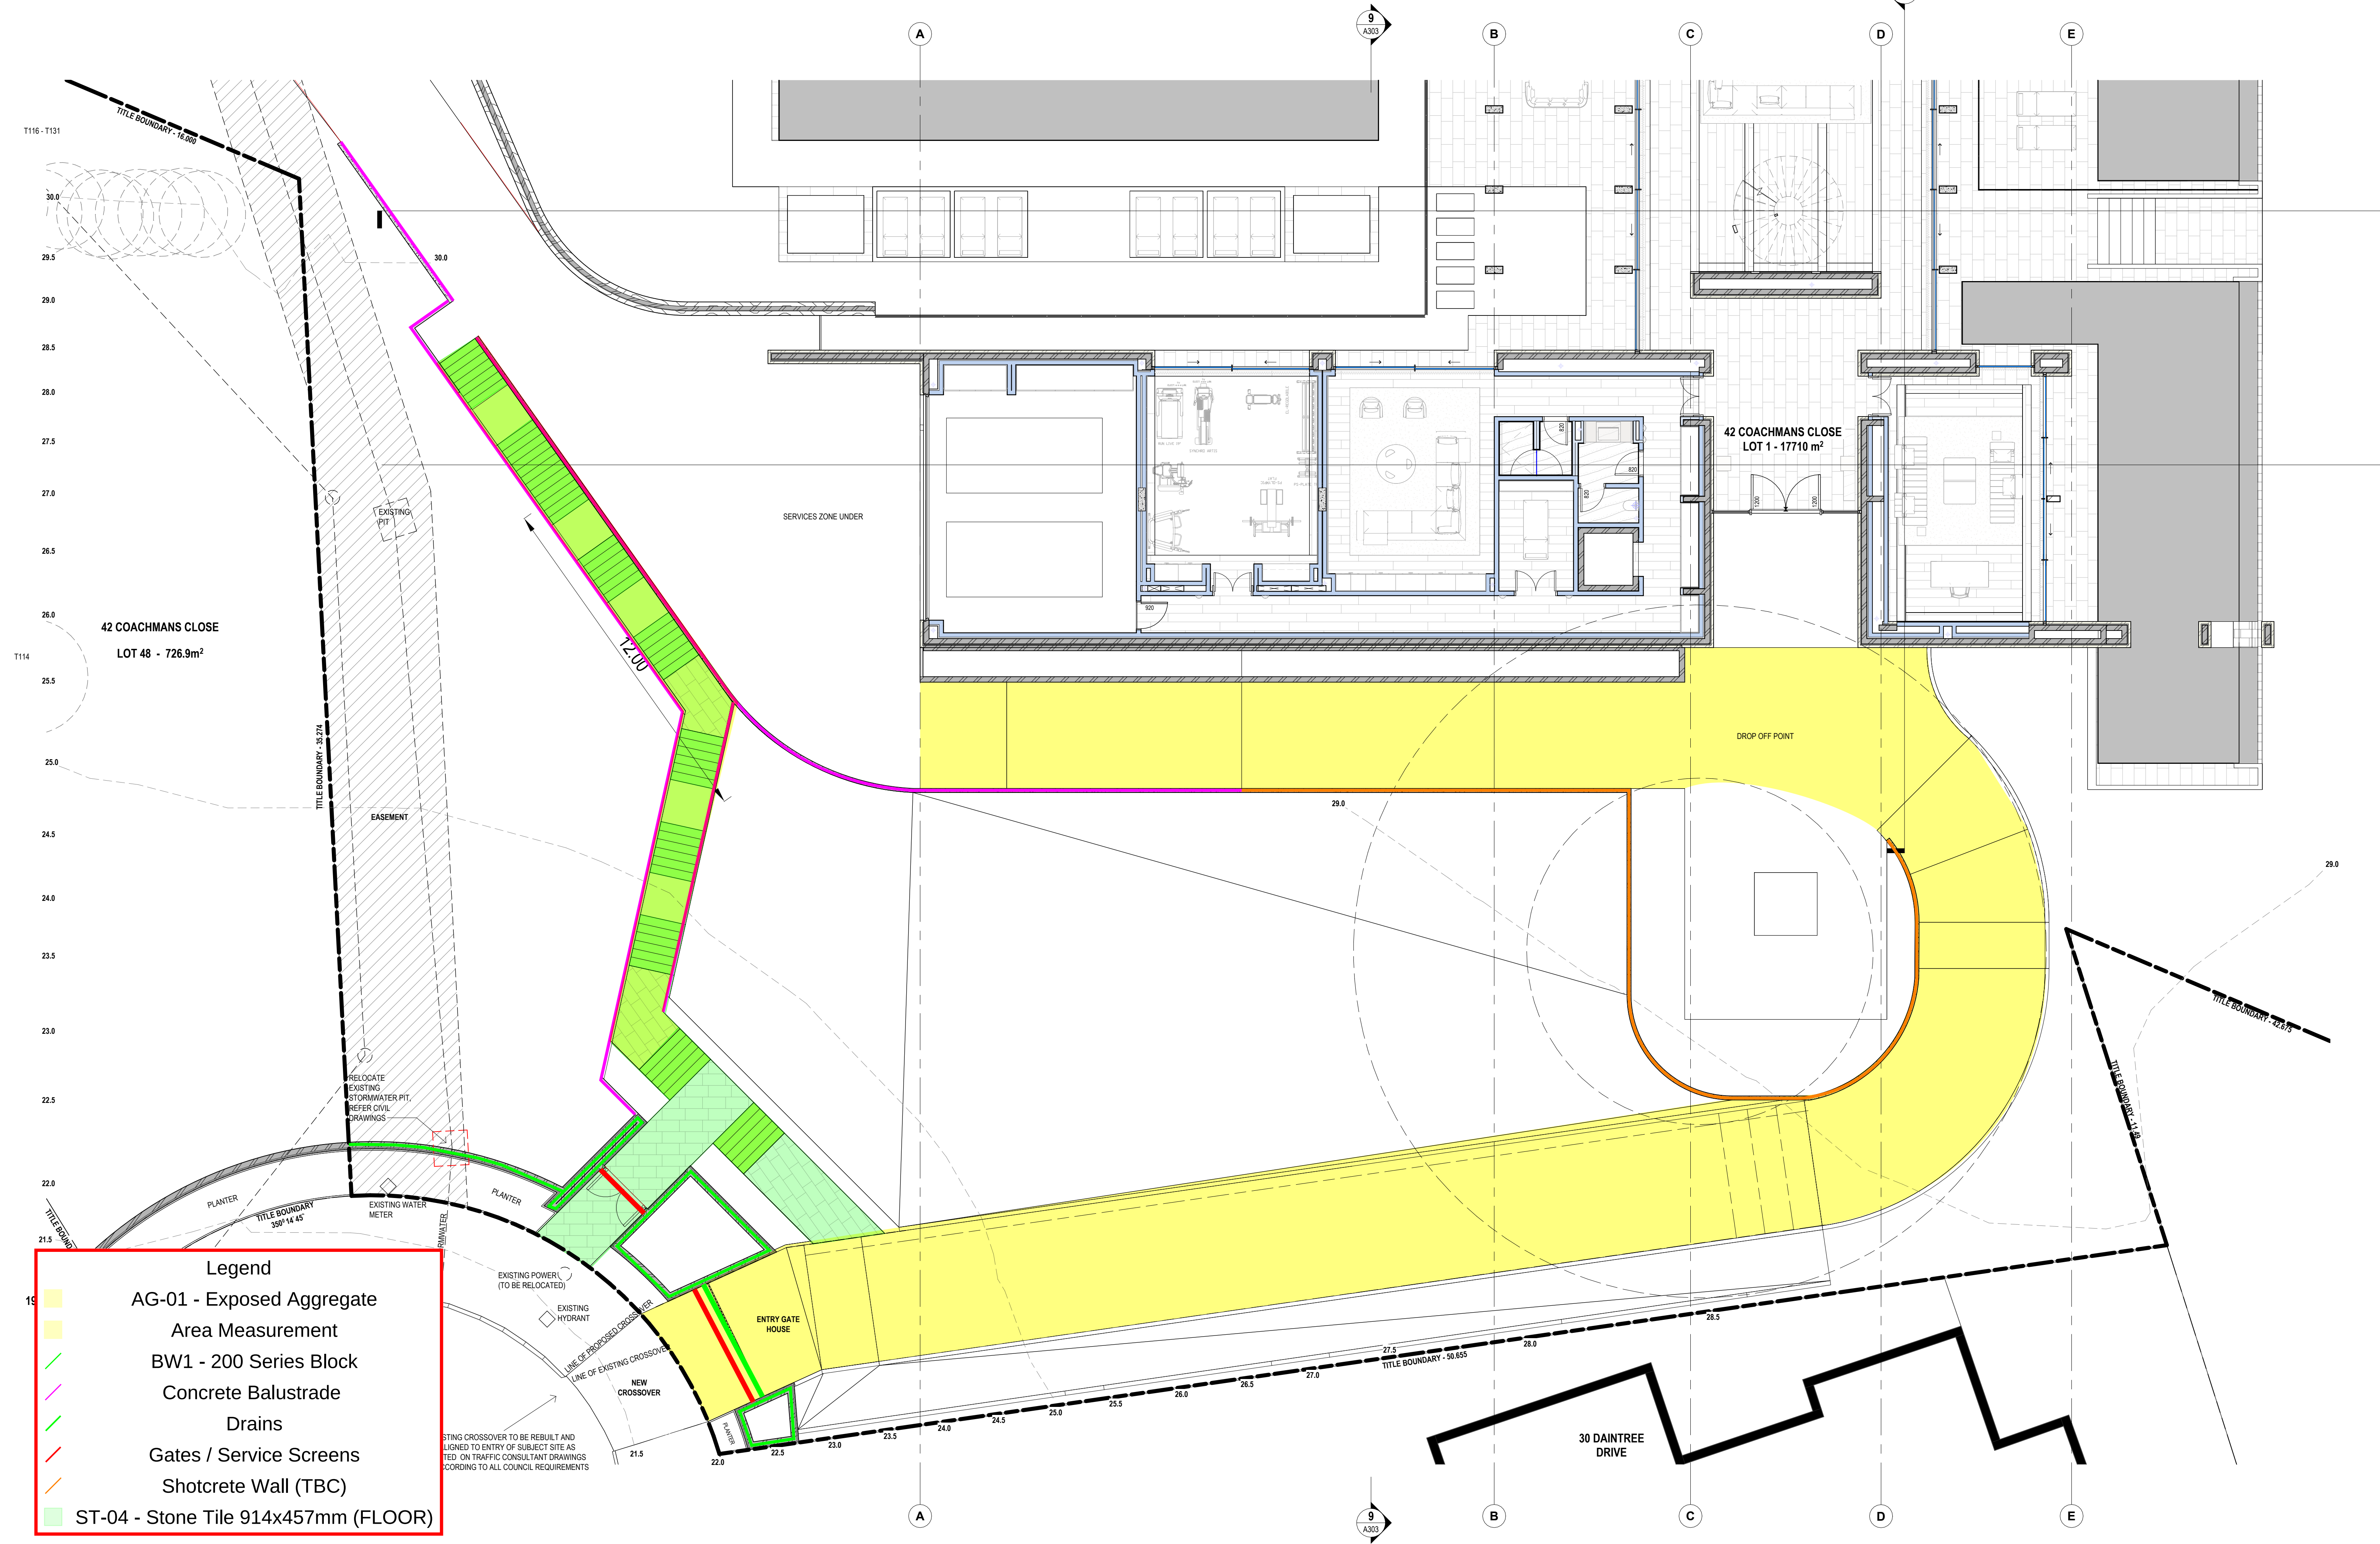

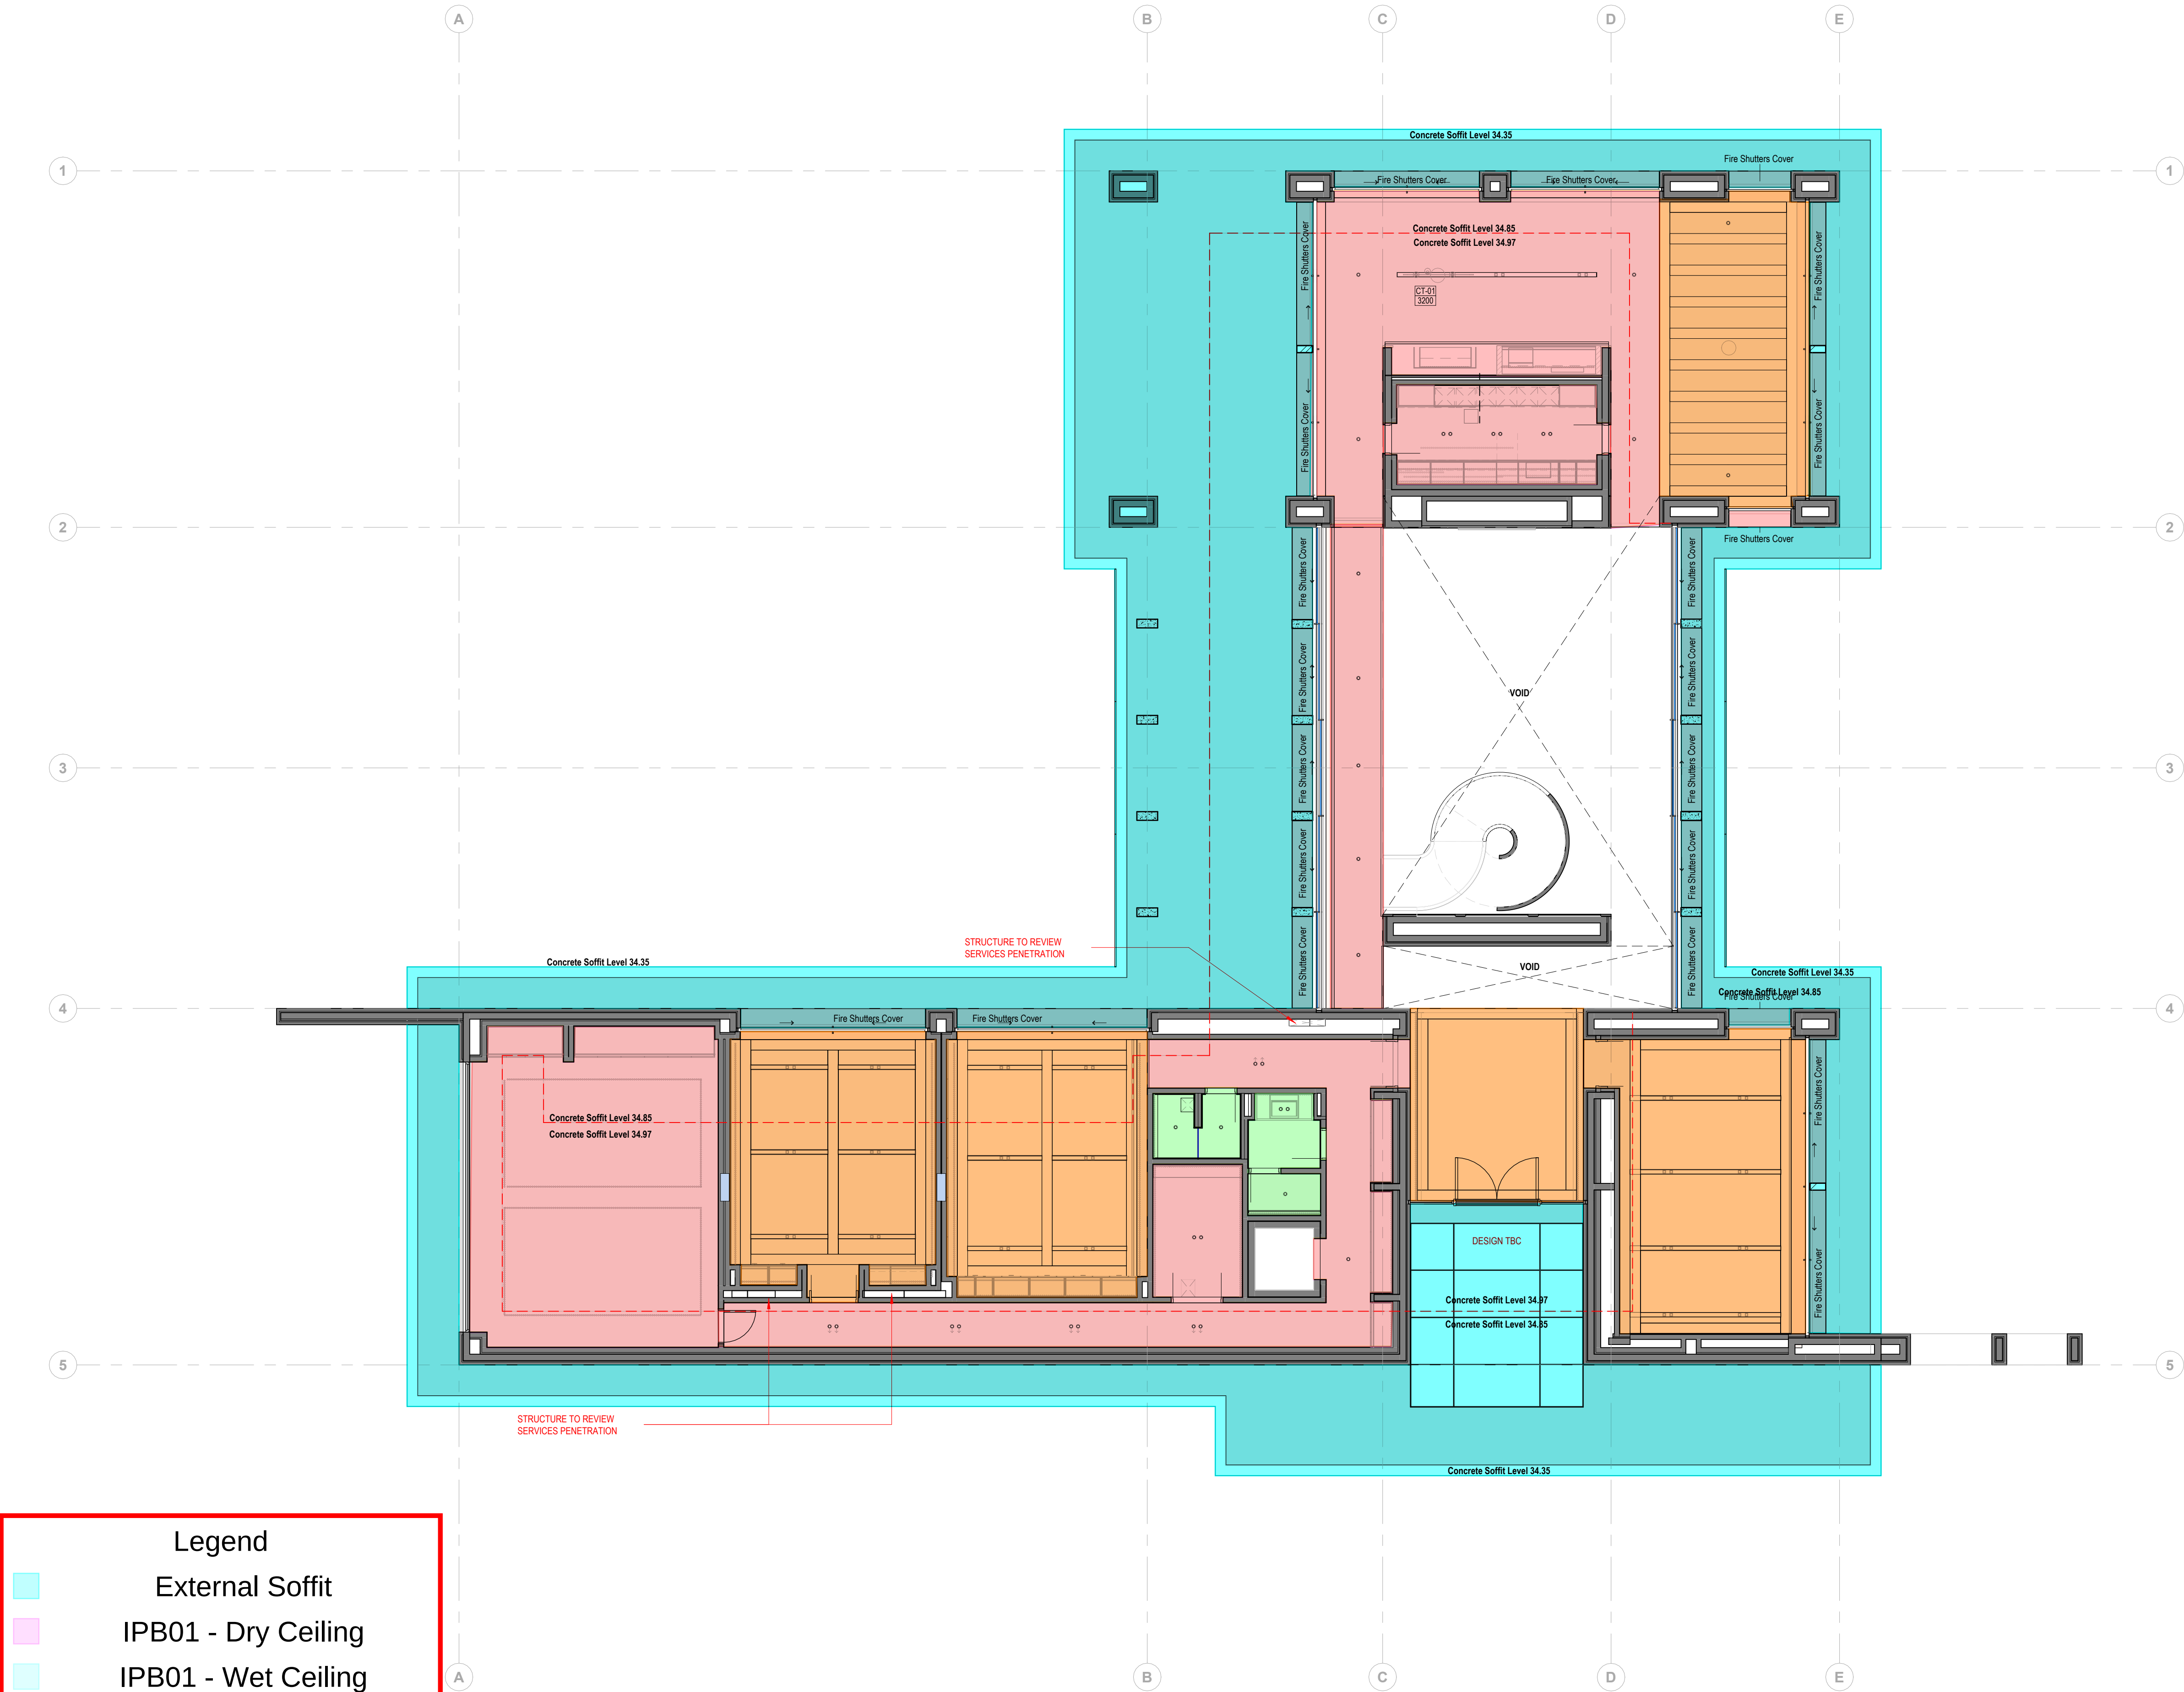

Legend

External Soffit

IPB01 - Dry Ceiling

IPB01 - Wet Ceiling

PT-02 - Dulux White (Ceiling)

Timber Ceiling



Legend

External Soffit

IPB01 - Dry Ceiling

IPB01 - Wet Ceiling

PT-02 - Dulux White (Ceiling)

Stone Ceiling

Timber Ceiling

Legend

AWS Aluminium System

- GENERAL NOTES:
- THIS PROJECT IS TO BE FZ COMPLIANT CONSTRUCTION IN ACCORDANCE AS3959 - 2018.
 - ALL GLAZED DOORS AND WINDOWS TO HAVE FZ COMPLIANCE SHUTTERS; REFER TO SHEET A8000 & A8001 FOR MORE INFORMATION.
 - USING VALUES FOR ALL WINDOWS ASSUME VICTROCSA DOUBLE GLAZED SYSTEM -- UW: 2.1 SHGC 0.32
 - ALL GLAZING TO COMPLY WITH AS 1288-2006.
 - ALL GLAZING TO WINDOWS IN BATHROOMS TO BE SAFETY GLASS AS PER AS 1288-2006
 - FLYSCREENS- RETRACTABLE FLYSCREENS TO SLIDING WINDOWS SPECIFICATION TBC. FIXED FLYSCREENS TO OTHER OPENABLE WINDOWS
 - DECALS TO CLAUSE 5.19 OF AS1288-2006. DECALS TBC. CONFIRMED PRIOR TO WINDOW MANUFACTURE
 - OPENABLE PORTION OF WINDOWS TO BE RESTRICTED IN ACCORDANCE WITH NCC REQUIREMENTS REFER SECTION H5P2.
 - ALL DIMENSIONS NOMINAL AND TBC ON SITE. SHOP DRAWINGS TO BE PROVIDED TO ARCHITECT FOR REVIEW PRIOR TO MANUFACTURE
 - GLAZING SYSTEMS ARE DRAWN AS VIEWED FROM OUTSIDE; REFER TO PLANS FOR SLIDING AND SWING DIRECTION
 - ALL USING VALUES AS PER ENERGY RATERS REPORT REQUIREMENTS (REFER TO SUMMARY BELOW)
 - ALL HEAD, SILL AND SIDE TRACKS TO BE RECESSED OR CONCEALED UNLESS NOTED OTHERWISE
 - SUBSILL AS PER MANUFACTURERS REQUIREMENTS AND DETAILS
 - DIMENSIONS ARE GENERALLY FOR VISIBLE EXTENTS OF WINDOWS UNLESS NOTED OTHERWISE
 - CONTRACTOR TO REVIEW ALL WINDOWS AND DETAILING FOR USE OF WINDOW BEAD ACCESS FOR GLASS REPLACEMENT
 - SUBSILLS TO INCLUDE SEPERATE DRAINAGE FOR ANY WATER ENTRY; DETAILS TBC WITH CONTRACTOR

53 4.095 OPENING 53		53 6.087 OPENING 53		53 1.800 OPENING 53		53 5.256 OPENING 53		1.500	
FIRST CL		FIRST CL		FIRST CL		FIRST CL		FIRST CL	
FIRST FFL		FIRST FFL		FIRST FFL		FIRST FFL		FIRST FFL	
WF.15, WF.17 2 Panel_Sliding FRAME FRAME FINISH GLAZING TYPE GLAZING FINISH OPERATION FLYSCREEN PERFORMANCE RATING SECURITY HARDWARE / LOCKING NOTES		WF.16 4 Panel 2 Track_Sliding Bi-Parting FRAME FRAME FINISH GLAZING TYPE GLAZING FINISH OPERATION FLYSCREEN PERFORMANCE RATING SECURITY HARDWARE / LOCKING NOTES		WF.18 Fixed FRAME FRAME FINISH GLAZING TYPE GLAZING FINISH OPERATION FLYSCREEN PERFORMANCE RATING SECURITY HARDWARE / LOCKING NOTES		WF.19 2 Panel_Sliding FRAME FRAME FINISH GLAZING TYPE GLAZING FINISH OPERATION FLYSCREEN PERFORMANCE RATING SECURITY HARDWARE / LOCKING NOTES		WF.20, WF.32 Fixed FRAME FRAME FINISH GLAZING TYPE GLAZING FINISH OPERATION FLYSCREEN PERFORMANCE RATING SECURITY HARDWARE / LOCKING NOTES	
3.250		2.656		4.350		4.400		8.500 OPENING	
FIRST CL		FIRST CL		FIRST CL		FIRST CL		FIRST CL	
FIRST FFL		FIRST FFL		FIRST FFL		FIRST FFL		FIRST FFL	
WF.21 Fixed FRAME FRAME FINISH GLAZING TYPE GLAZING FINISH OPERATION FLYSCREEN PERFORMANCE RATING SECURITY HARDWARE / LOCKING NOTES		WF.22 Fixed FRAME FRAME FINISH GLAZING TYPE GLAZING FINISH OPERATION FLYSCREEN PERFORMANCE RATING SECURITY HARDWARE / LOCKING NOTES		WF.23 Fixed FRAME FRAME FINISH GLAZING TYPE GLAZING FINISH OPERATION FLYSCREEN PERFORMANCE RATING SECURITY HARDWARE / LOCKING NOTES		WF.24 Fixed FRAME FRAME FINISH GLAZING TYPE GLAZING FINISH OPERATION FLYSCREEN PERFORMANCE RATING SECURITY HARDWARE / LOCKING NOTES		WF.25 4 Panel 2 Track_Sliding Bi-Parting FRAME FRAME FINISH GLAZING TYPE GLAZING FINISH OPERATION FLYSCREEN PERFORMANCE RATING SECURITY HARDWARE / LOCKING NOTES	
2.855		13.950		4.112 OPENING		4.210		1.500	
FIRST CL		FIRST CL		FIRST CL		FIRST CL		FIRST CL	
FIRST FFL		FIRST FFL		FIRST FFL		FIRST FFL		FIRST FFL	
WF.26 Fixed FRAME FRAME FINISH GLAZING TYPE GLAZING FINISH OPERATION FLYSCREEN PERFORMANCE RATING SECURITY HARDWARE / LOCKING NOTES		WF.27, WF.28 2 Panel_Sliding FRAME FRAME FINISH GLAZING TYPE GLAZING FINISH OPERATION FLYSCREEN PERFORMANCE RATING SECURITY HARDWARE / LOCKING NOTES		WF.29 Fixed FRAME FRAME FINISH GLAZING TYPE GLAZING FINISH OPERATION FLYSCREEN PERFORMANCE RATING SECURITY HARDWARE / LOCKING NOTES		WF.30, WF.31 Fixed FRAME FRAME FINISH GLAZING TYPE GLAZING FINISH OPERATION FLYSCREEN PERFORMANCE RATING SECURITY HARDWARE / LOCKING NOTES			
2.855		3.000 OPENING		3.000 OPENING		3.000 OPENING		3.000 OPENING	
FIRST CL		FIRST CL		FIRST CL		FIRST CL		FIRST CL	
FIRST FFL		FIRST FFL		FIRST FFL		FIRST FFL		FIRST FFL	

Legend

AWS Aluminium System

- GENERAL NOTES:
1.

THIS PROJECT IS TO BE FZ COMPLIANT CONSTRUCTION IN ACCORDANCE AS3959 - 2018.
2.
- ALL GLAZED DOORS AND WINDOWS TO HAVE FZ COMPLIANCE SHUTTERS; REFER TO SHEET A8000 & A8001 FOR MORE INFORMATION.

3.

4.

5.

6.

7.

8.

9.

10.

11.

12.

13.

14.

15.

16.